

ŚCIANY ZEWNĘTRZNE – GAZOBETON TYPU 590/240 ODMIANY 500 gr. 24 [cm] – WARSTWA NOŚNA
OCIEPLENIE – STYROPIAN gr. 20 [cm]

OD WEWNĄTRZ ŚCIANY OTYKOWANE TYNKIEM CEM. – WAP. KAT III
SPOINA MARKI M3 – 3 [MPa]

WENTYLACJA MECHANICZNA Z REKUPERACJĄ W OBIEKCIE WG ODDZIELNEGO OPRAWOWANIA

WENTYLACJA WSPOMAGANA MECHANICZNIE

RZUT PARTERU - architektura


1:100

BUDYNEK MIESZKALNY

pow. użytkowa (mieszkalna) /m2/: 120,03
pow. użytkowa /m2/: 168,03
pow. zabudowy /m2/: 213,14
kubatura /m3/: 932,80
wysokość do kalenicy /m /: 8,00

PARTER – WYKAZ POMIESZCZEŃ			
Nr	pomieszczenie	posadzka	pow. użytkowa (mieszkalno)/m2/ użytkowo/m2/
01	WATROZAP	terakota	3,97
02	HOL	panele	8,46
03	POKÓJ GOŚCINNY	terakota	12,57
04	ŁAZIENKA	panele	4,42
05	GABINET	panele	12,73
06	SALON Z KUCHNIĄ	panele	46,43
07	SPIŻARNIA	terakota	5,17
08	SYPIALNIA	panele	17,04
09	GARDEROBA	panele	4,22
10	ŁAZIENKA	panele	5,02
11	GARAŻ	terakota	0,00
RAZEM powierzchnia			120,03
pow. całkowita parteru /m2/:			168,03

ŻELBETOWY SŁUP/RODZEŃ 24x24[cm] Z BET. C16/20(B20)
ZBRÓJONY 4x12 STRZEMIOMA Ø6 CO 15 cm
DŁUGOŚĆ ZAKOTWIENIA ZBRÓJENIA GŁÓWNEGO
W STROPIE l=50 cm

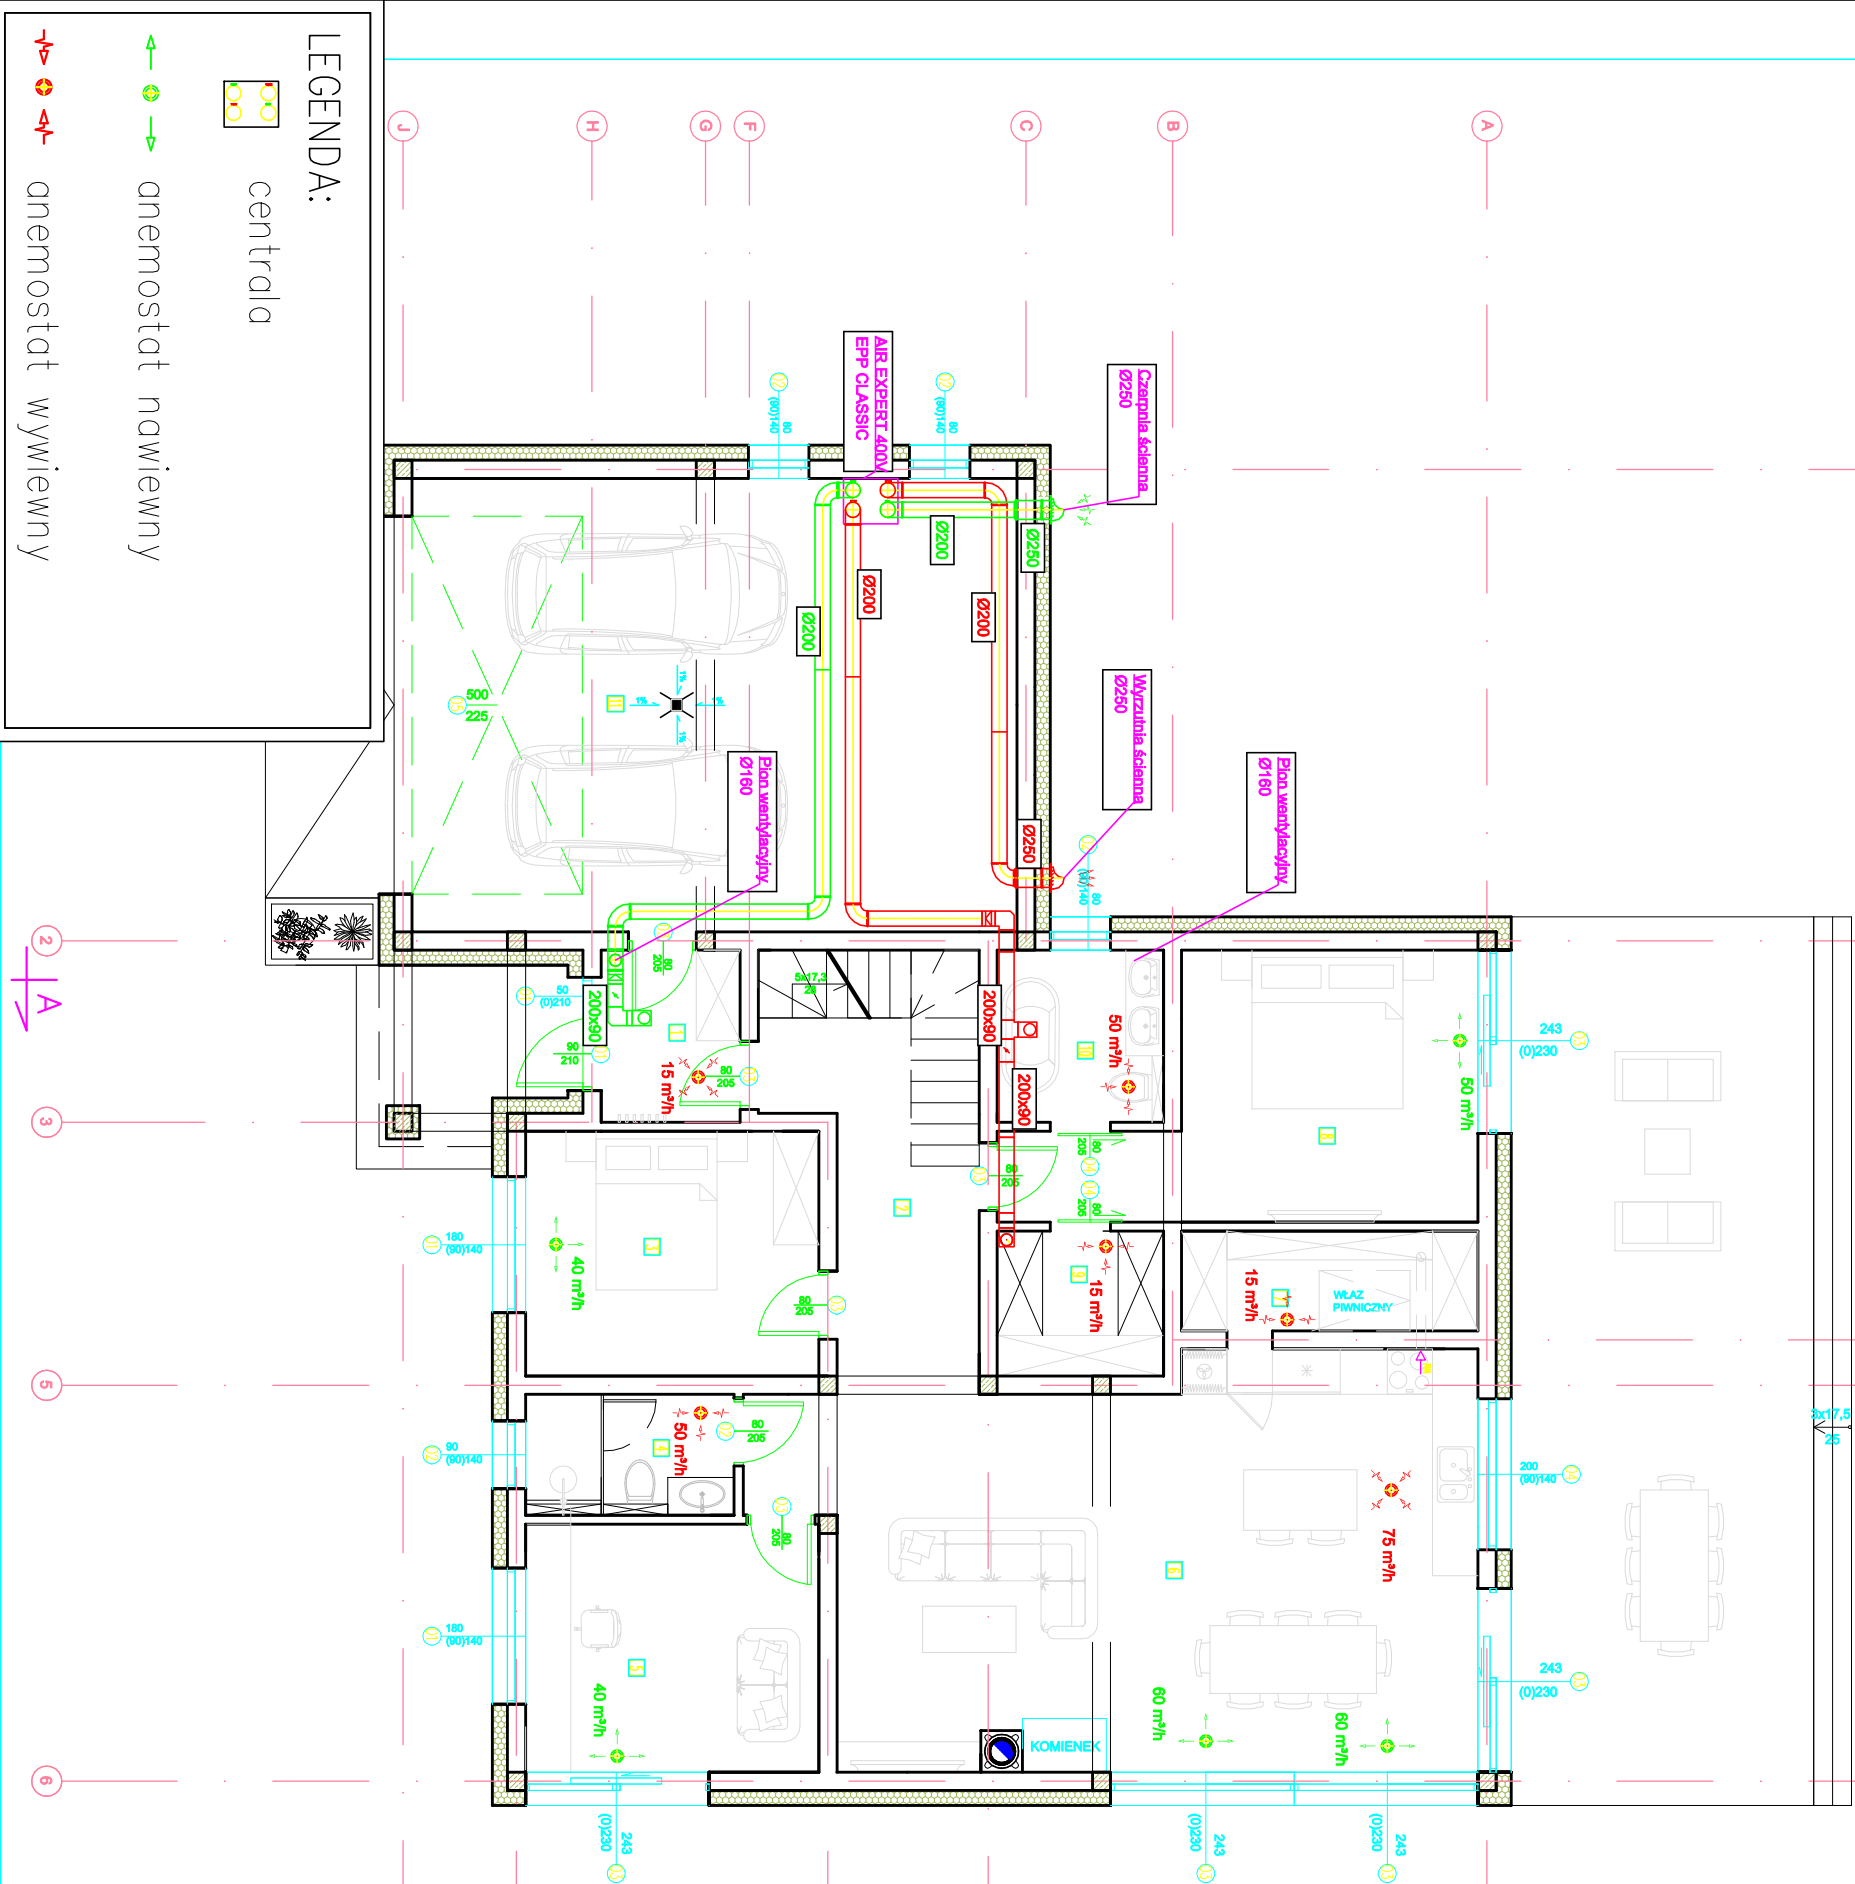

Projekt:	BUDYNEK MIESZKALNY JEDNORODZINNY		
Investor:			
Adres inwestycji:			
Data:	01-2024	Skala:	1:100
Nr Rys.	1		
Projektant:	Sebastian Leszczyński		
Tytuł rysunku:	PROJEKT WENTYLACJI MECHANICZNEJ Z ODDZYSKIEM CIEPŁA PARTER ANEMOSTATY		